
PROCESS FLOW & LAYOUT

4 TPH COOKED TUB PLANT — VAN BUREN, ARKANSAS

Ref. proposal MCE-Q-2610-FCO-R1 · October 20, 2026 · Sheet 1 of 2

PLAN VIEW — PROPOSED ARRANGEMENT

Approximate scale, for discussion — not for construction

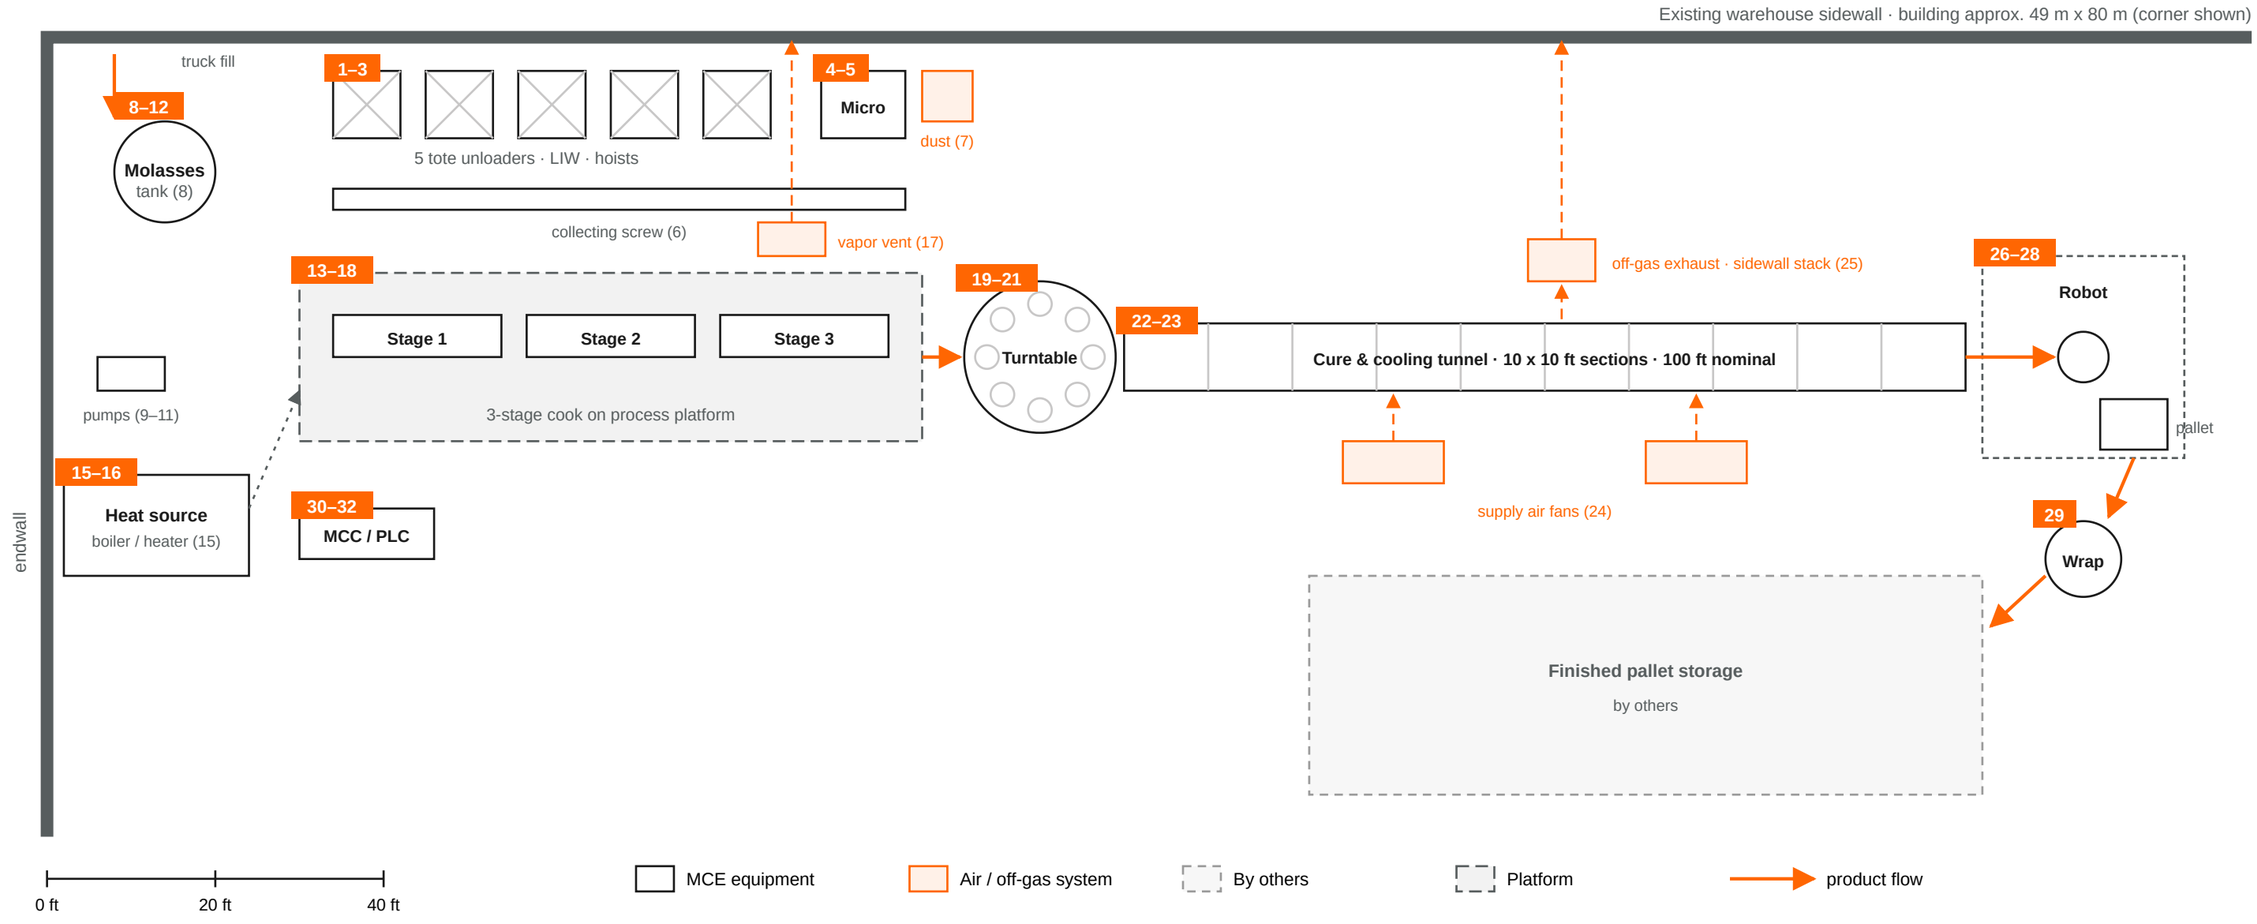


Orange tags are the item numbers in proposal MCE-Q-2610-FCO-R1. The plant sits in one corner of the existing Van Buren warehouse. Totes, the micro skid and molasses feed a 3-stage cook on a process platform; hot product pours into tubs on the rotary turntable, cures through a 100 ft forced-air tunnel with off-gas exhausted out the sidewall, and is stacked by the robot and stretch wrapped. Equipment locations, tunnel length, conveyor lengths and elevations to be confirmed in FEED.


PROCESS FLOW DIAGRAM

4 TPH (8,000 lb/hr) rated · cooked low-moisture protein tubs


DRY INGREDIENTS & MOLASSES · 4 TPH (8,000 lb/hr) rated

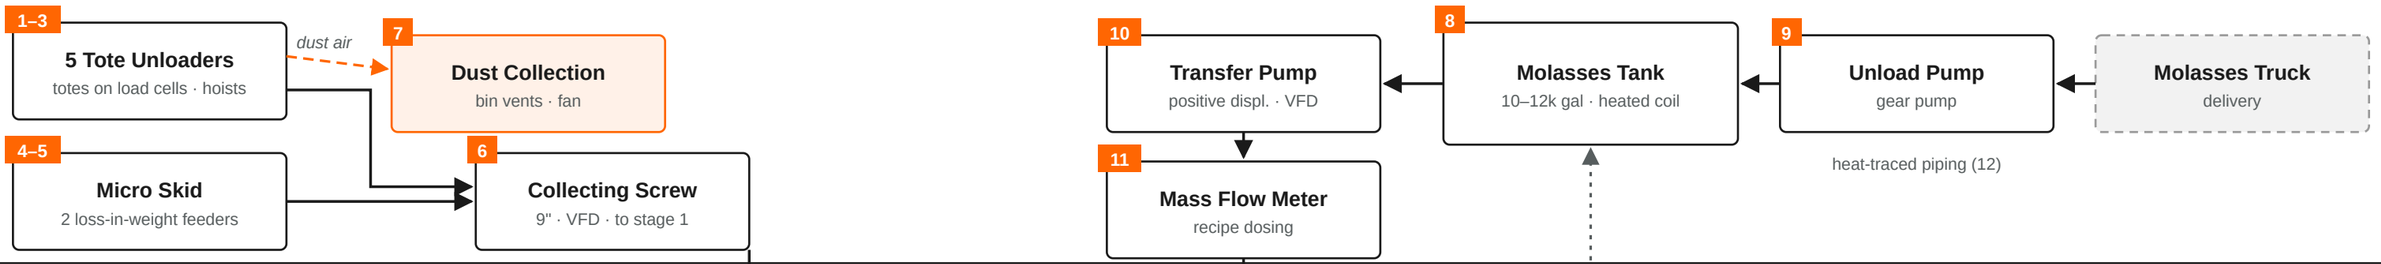


3-STAGE COOK SYSTEM · MCE design

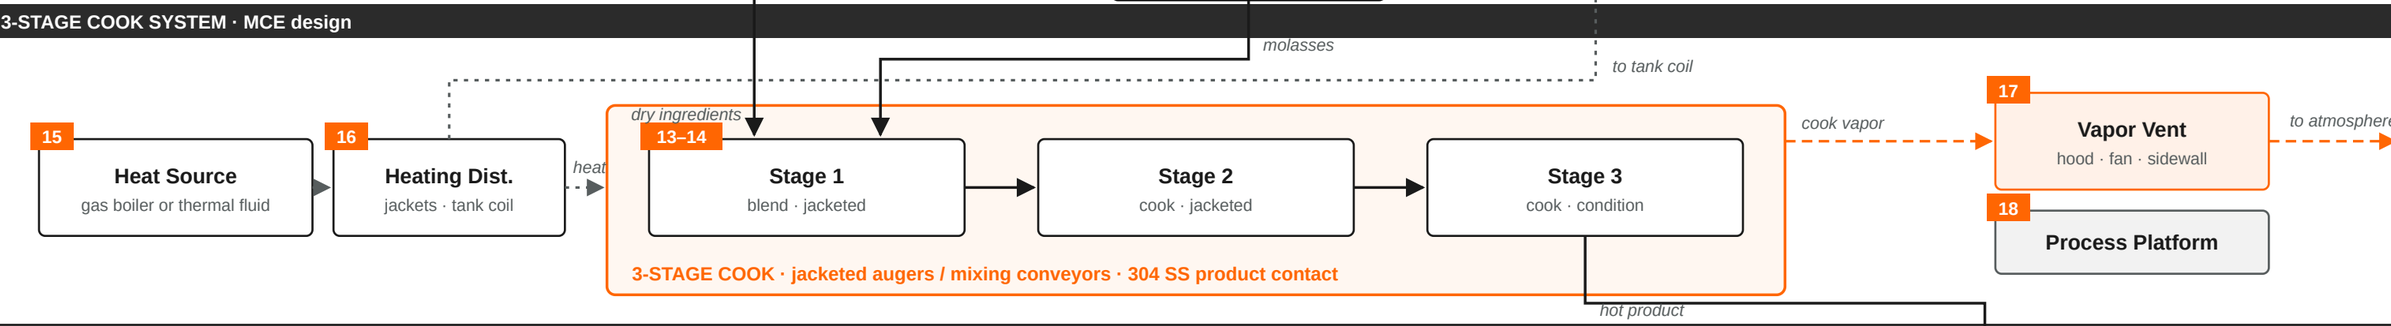

POUR, CURE & COOL

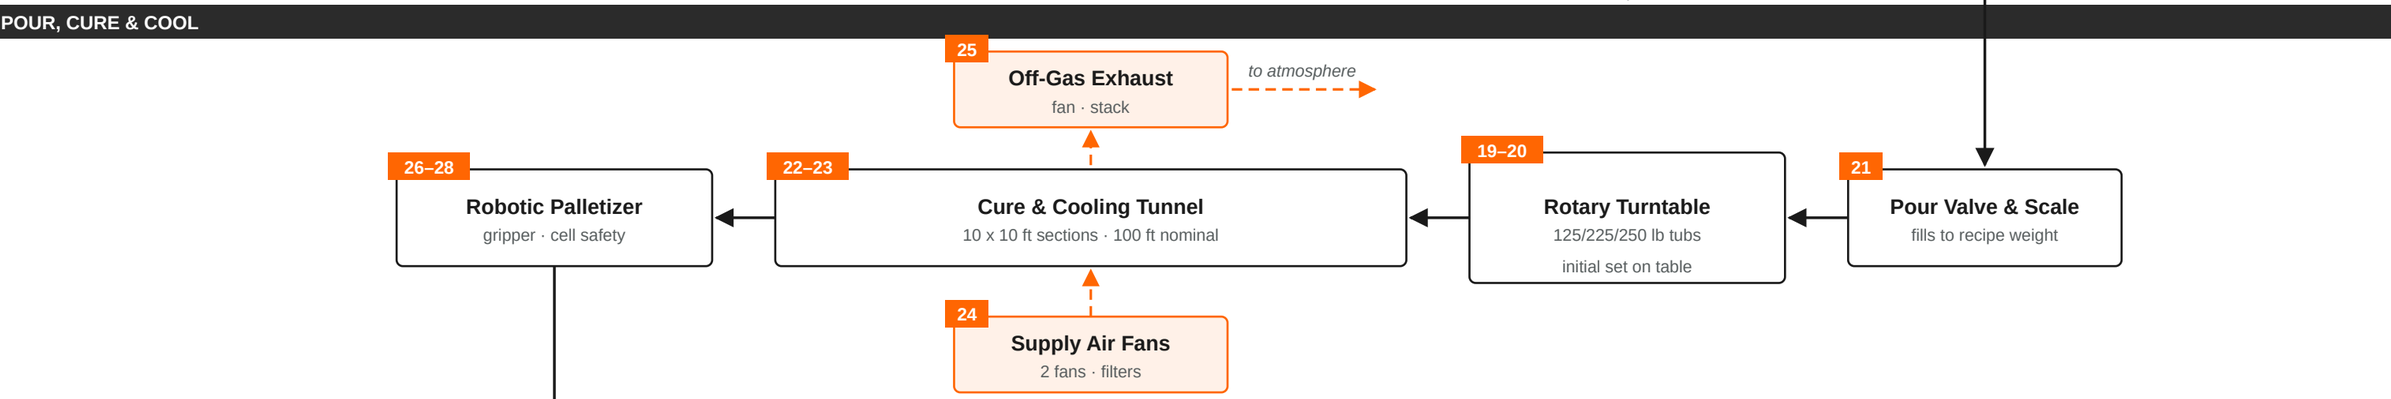

STACK, WRAP & PLANT CONTROLS

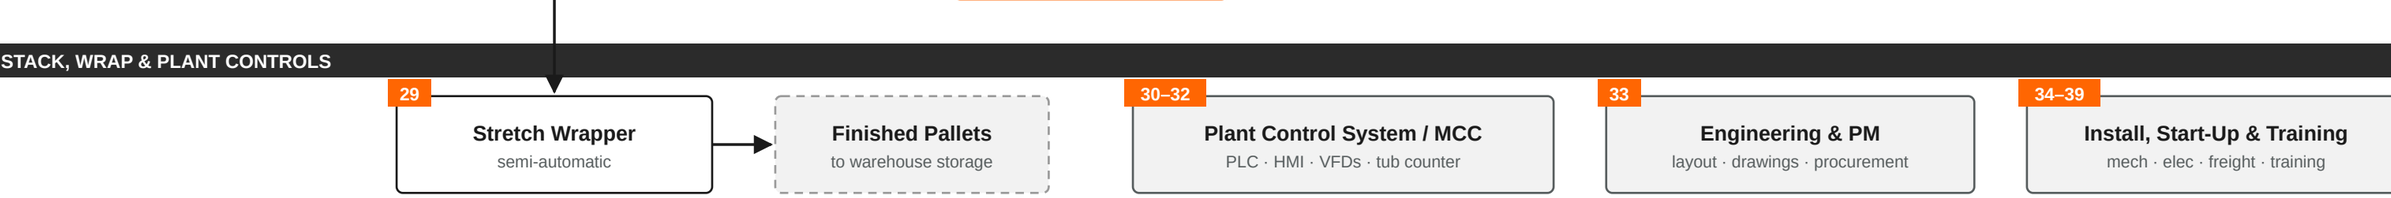

Solid lines = product flow · dashed orange = air / off-gas systems · dotted grey = heat · dashed grey boxes = by others · orange tags = proposal item numbers.